
LEGENDA LUMINOTÉCNICA - FORRO

SÍMBOLO	DESCRIÇÃO	ALTURA	QUANT.
	PERFIL DE LED DE EMBUTIR 10mm 3.000K | ACAB.: BRANCO #AMBIENTES:MARCENARIA	MARCENARIA	6.10m
	PERFIL DE LED DE SOBREPOR 36mm 3.000K | ACAB.: BRANCO #AMBIENTES: SUÍTE	FORRO	5.00m
	PERFIL T LED SOBREPOR 3M 3.000K | ACAB.: BRANCO #AMBIENTES: SUÍTE	FORRO	3.00m
	PERFIL T LED SOBREPOR 2M 3.000K | ACAB.: BRANCO #AMBIENTES: QUARTO VISITAS	FORRO	2.00m
	SPOT PICO 03 FOCOS 3.000K | ACAB.: BRANCO #AMBIENTE: SALA DE ESTAR	FORRO	04 UNI
	SPOT DE SOBREPOR REDONDO 3000K | ACAB.: BRANCO #AMBIENTE: ÁREA GOURMET	FORRO	04 UNI
	PENDENTE A DEFINIR 3.000K | ACAB.: A DEFINIR #AMBIENTE: SALA DE JANTAR, Á. GOURMET	FORRO	03 UNI

OBS: TODOS OS EMBUTIDOS E SPOTS COM FOCO RECUADO;

LEGENDA LUMINOTÉCNICA - PAREDE

SÍMBOLO	DESCRIÇÃO	ALTURA	QUANT.
	PONTO DE ELÉTRICO P/ FITA/PERFIL DE LED 3.000K | ACAB.: BRANCO #AMBIENTES: COZINHA, VARANDA, SALA, Q. REVERSÍVEL E SUÍTE	CONFERIR NO DESENHO	03 UNI
	PONTO PARA ESPELHO ILUMINADO ILUMINAÇÃO 3.000K #AMBIENTE: SUÍTE	1.40m	01 UNI
	PONTO PARA ARANDELA 3.000K | ACAB.: À DEFINIR #AMBIENTE: SALA, Q. REVERSÍVEL E SUÍTE	1.20m	04 UNI

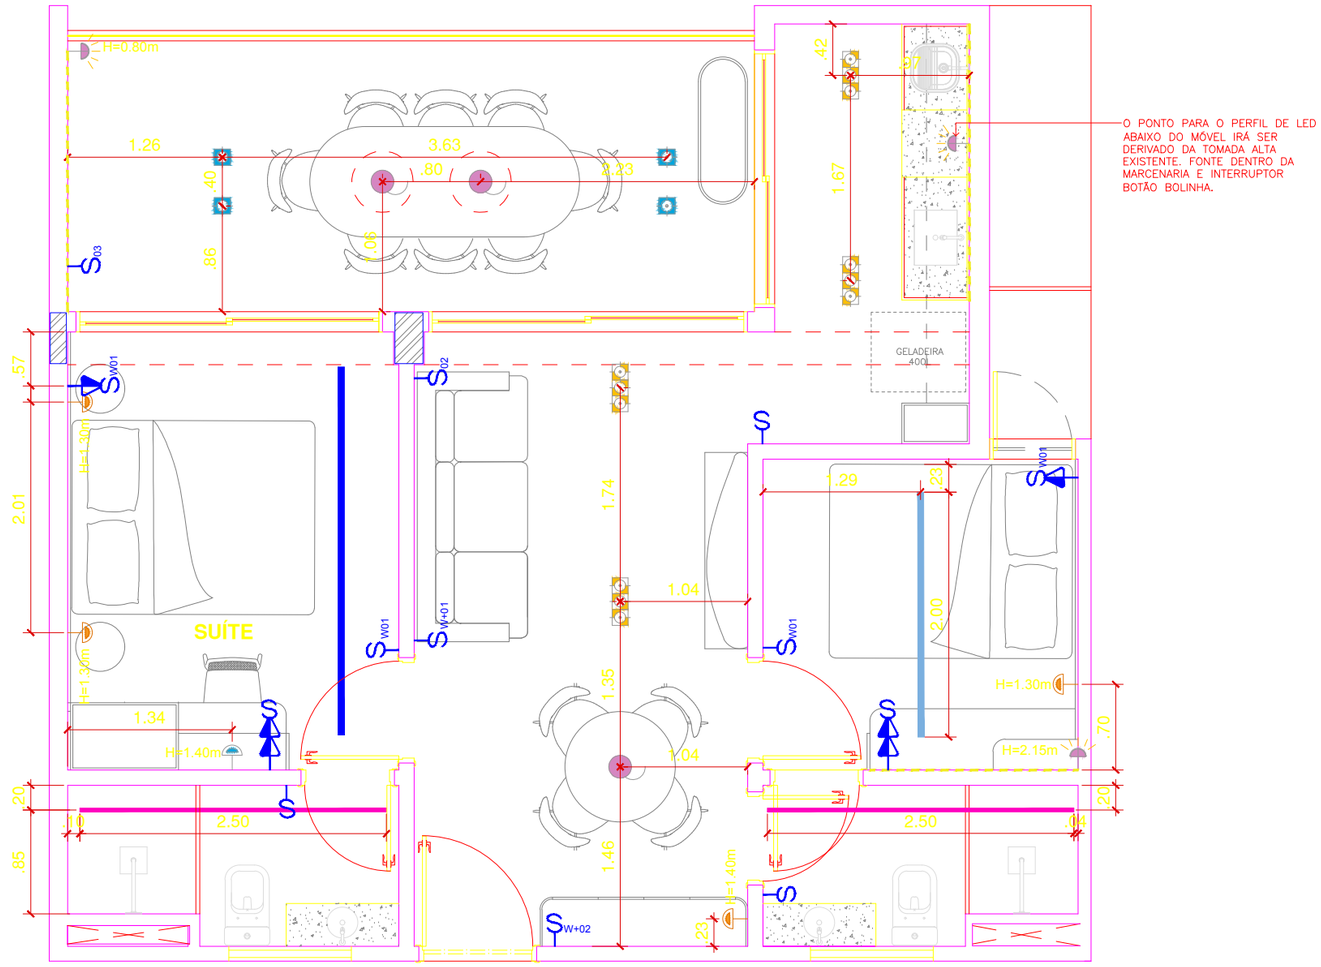

PLANTA DE PONTOS LUMINOTÉCNICOS
ESC 1/50

ANA LU arquitetura de interiores

Rua Professora Maria Esther da Costa Barros, n°246, sala 05,Jatiúca. Contato (82) 99601-9002.
escritoriolc@gmail.com

ASSUNTO:

PROJETO DE INTERIORES APTO 209 - TORRE SUL

CONTEÚDO:

PLANTA DE PONTOS LUMINOTÉCNICOS

ENDEREÇO:

Milagres Beach Residence - São Miguel dos Milagres. AL.

CLIENTE:

CARLOS HENRIQUE

DESENHO

DESENHO

REVISÃO 01

DATA
FEVEREIRO/2026

ESCALA
1/50

PRANCHA Nº

05/07

*TODAS AS MEDIDAS DEVEM SER CONFERIDAS NO LOCAL.

IMPRIMIR EM A3 1/50